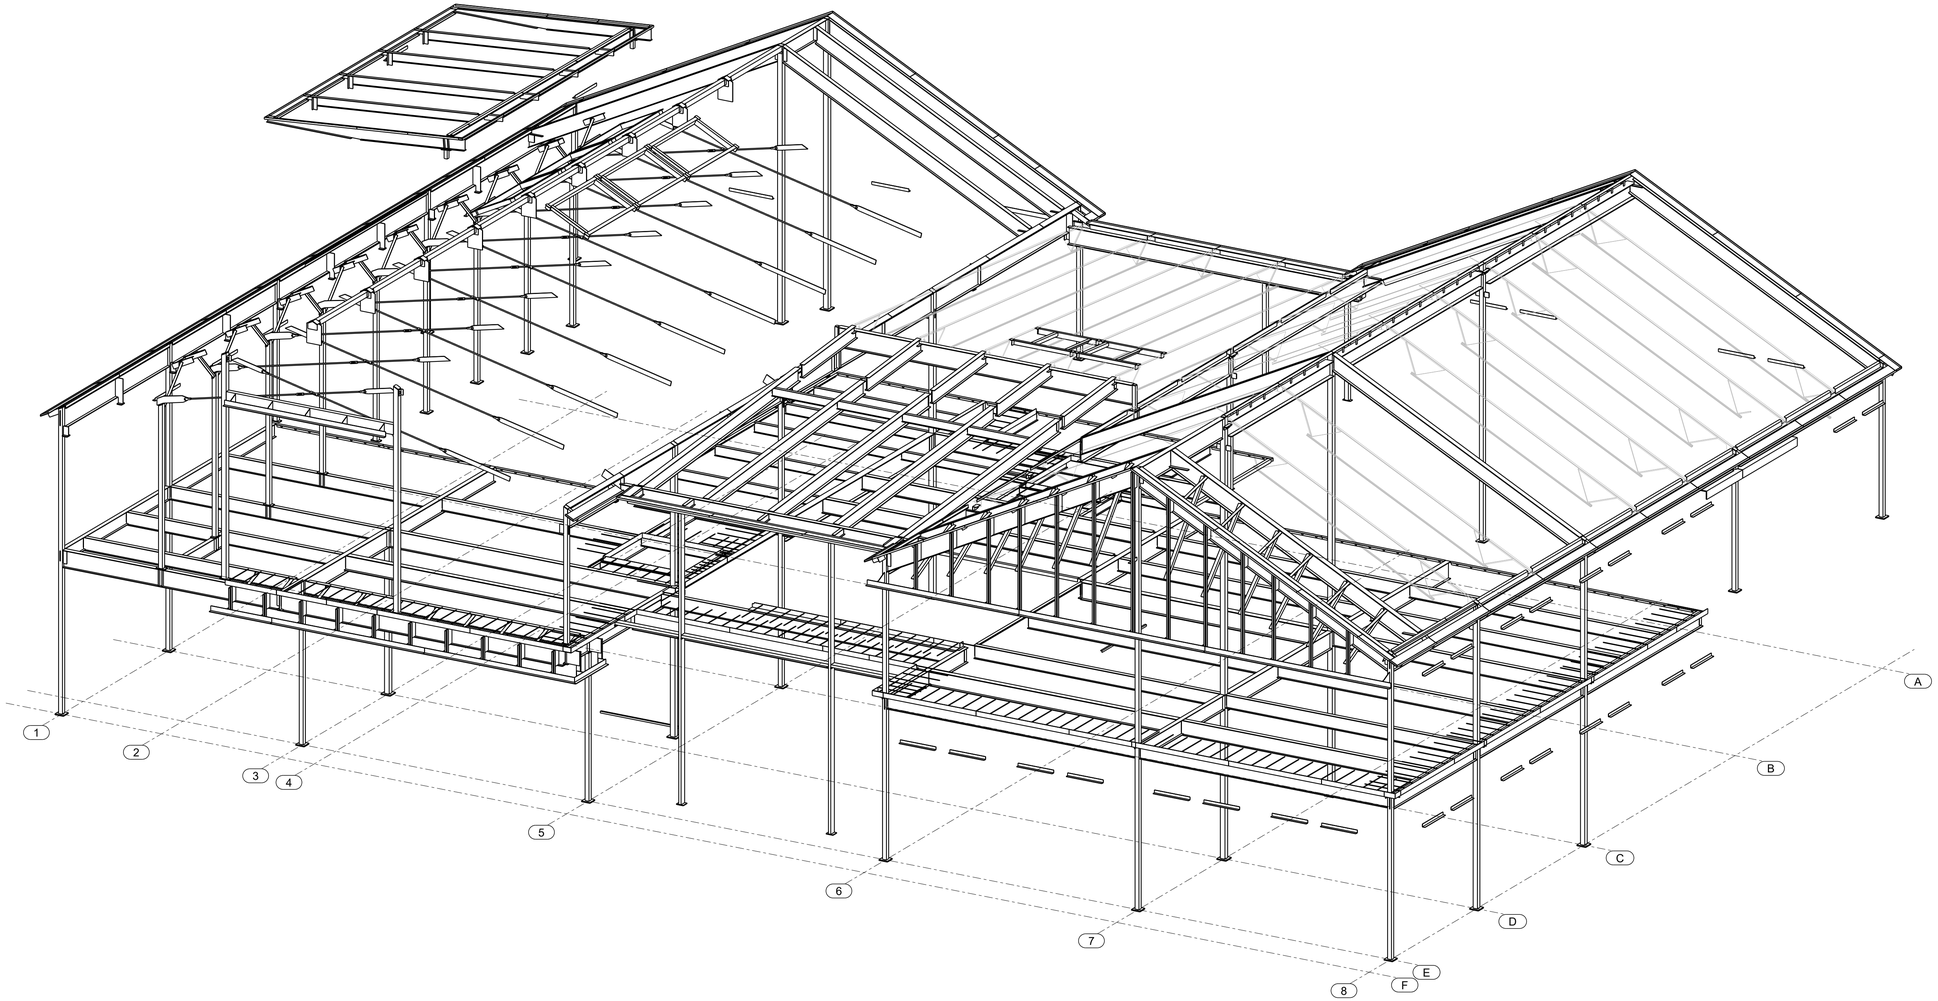


3D VIEW

Release 7

REV	DATE	BY	DESCRIPTION
0	06/22/2026	CAP	FOR FIELD USE
A	04/08/2026	CAP	FOR APPROVAL


SPOKANE METALS
STEEL FABRICATORS

18515 Garland Ave
Spokane Valley, WA 99027

DWG NAME: 3D VIEW
FOR Morrow Court House
LOCATION 640 NE COURTHOUSE WAY
CONTRACTOR Bouton Construction Company
DRAWN 02/12/2026 BY YRM CHECKED 06/22/2026 BY ASC

CONT. NO.	DWG. NO.
26-09	E300

Tekla Structures

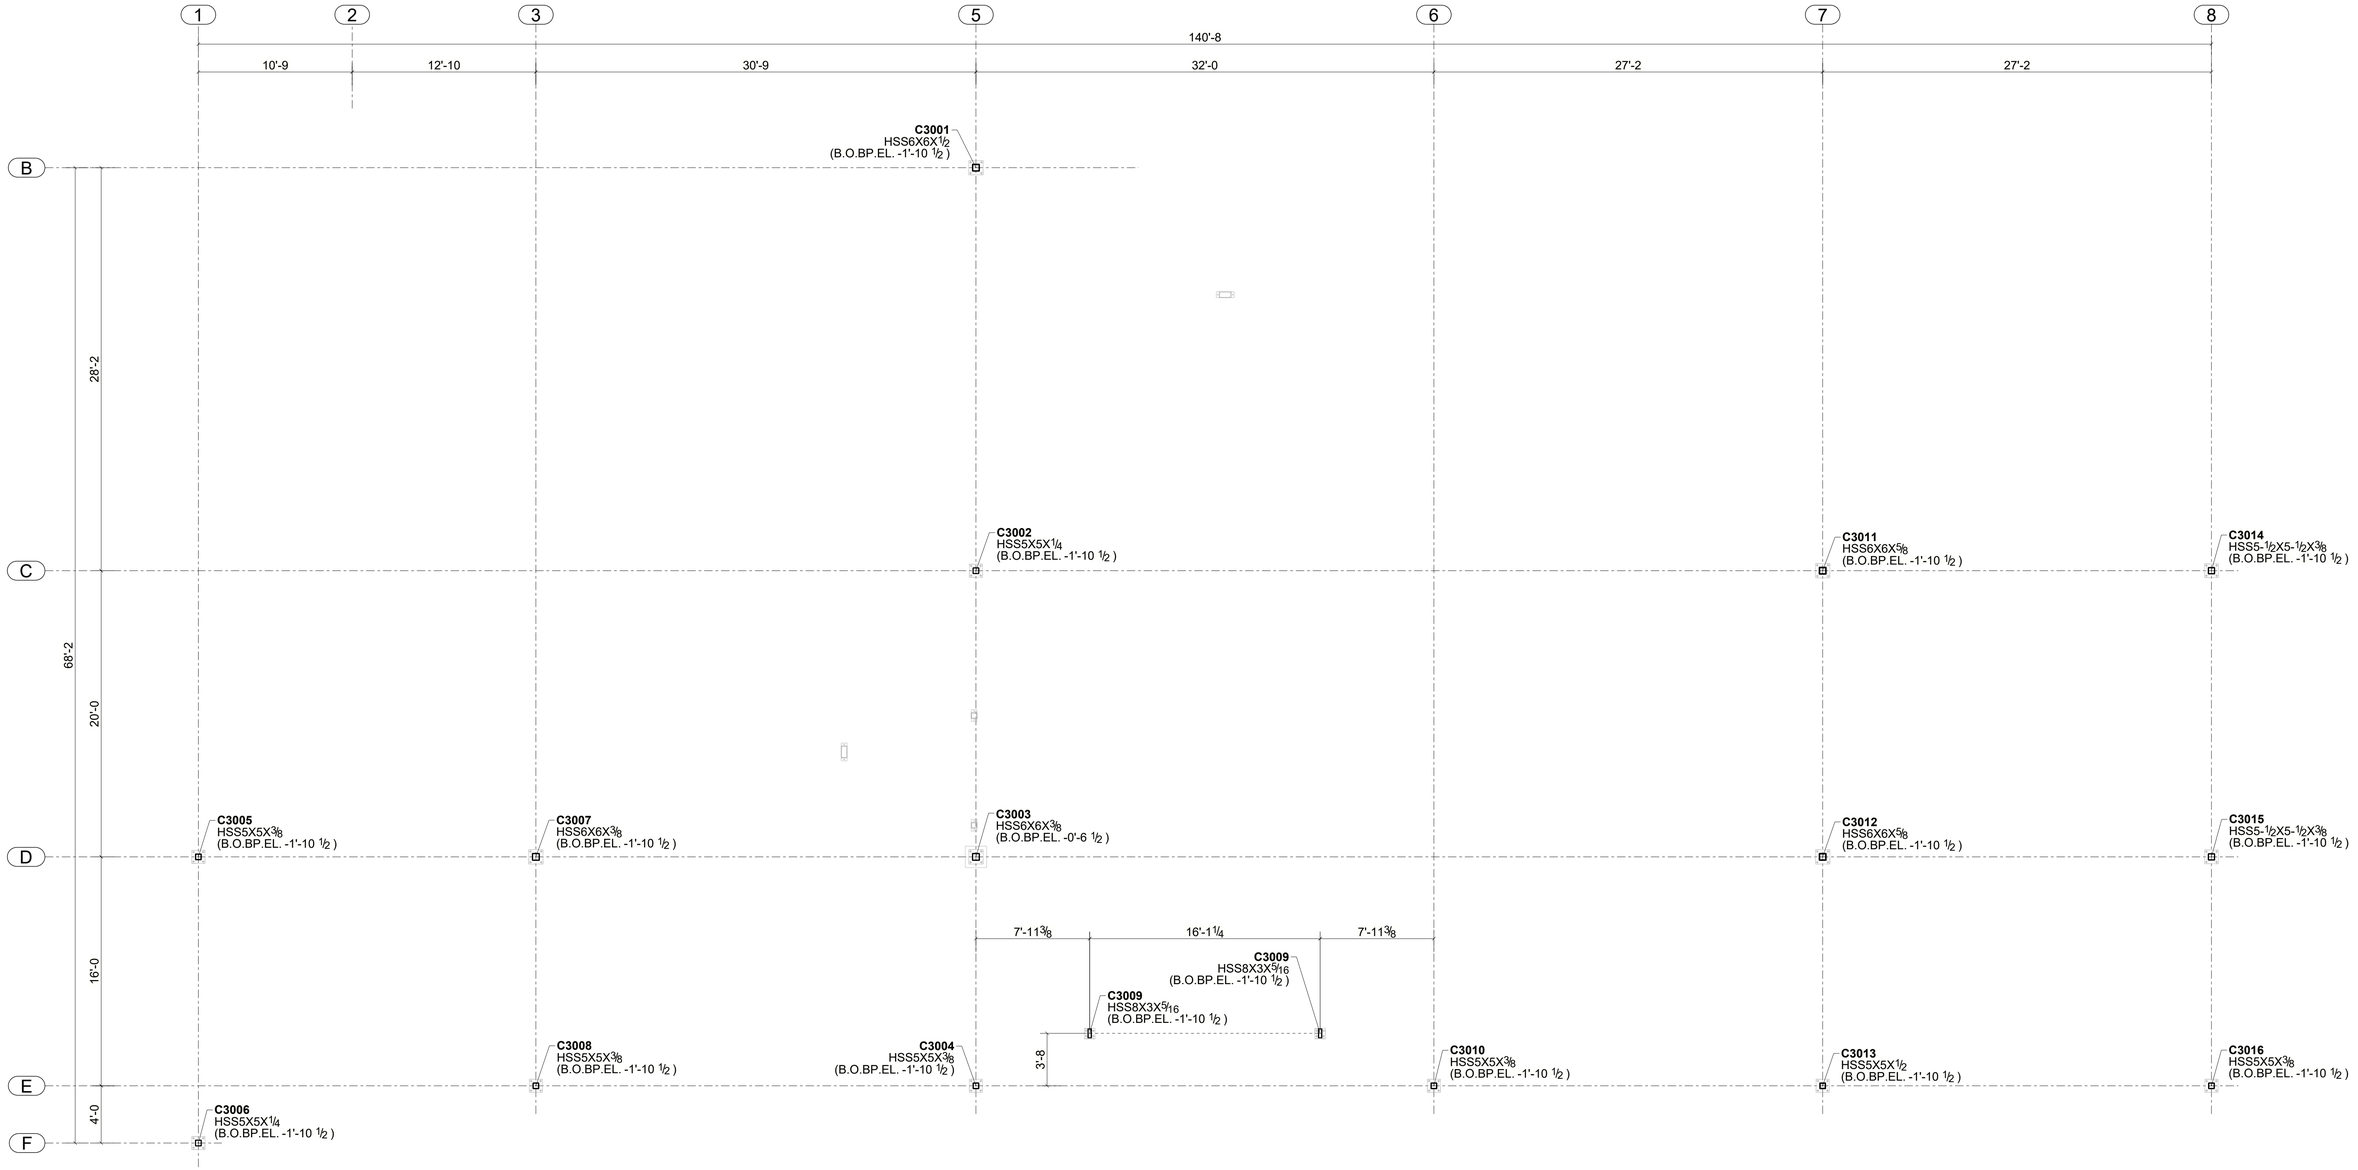


FOUNDATION COLUMN PLAN

(REF.: S1.1)

Release 7

REV	DATE	BY	DESCRIPTION
0	06/22/2026	CAP	FOR FIELD USE
A	04/08/2026	CAP	FOR APPROVAL

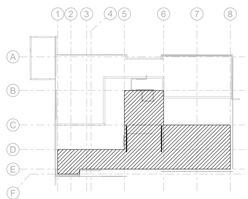

KEY PLAN

LEGEND:-

B.O.BP. - BOTTOM OF BASE PLATE
EL. - ELEVATION

SPOKANE METALS
STEEL FABRICATORS
18515 Garland Ave
Spokane Valley, WA 99027

DWG NAME: FOUNDATION COLUMN PLAN
FOR Morrow Court House
LOCATION 640 NE COURTHOUSE WAY
CONTRACTOR Bouton Construction Company
DRAWN 02/12/2026 BY YRM CHECKED 06/22/2026 BY ASC

CONT. NO.	DWG. NO.
26-09	E301

Tekla Structures



KEY PLAN

LEGEND:-

B.O.BP.	-	BOTTOM OF BASE PLATE
EL.	-	ELEVATION

LEVEL 2 COLUMN PLAN
(REF.: S1.2)

Release 7

REV	DATE	BY	DESCRIPTION
0	06/22/2026	CAP	FOR FIELD USE
A	04/08/2026	CAP	FOR APPROVAL


SPOKANE METALS
STEEL FABRICATORS


18515 Garland Ave
Spokane Valley, WA 99027

DWG NAME: LEVEL 2 COLUMN PLAN
FOR Morrow Court House
LOCATION 640 NE COURTHOUSE WAY
CONTRACTOR Bouton Construction Company
DRAWN 02/12/2026 BY YRM CHECKED 06/22/2026 BY ASC

CONT. NO.	DWG. NO.
26-09	E302

Tekla Structures

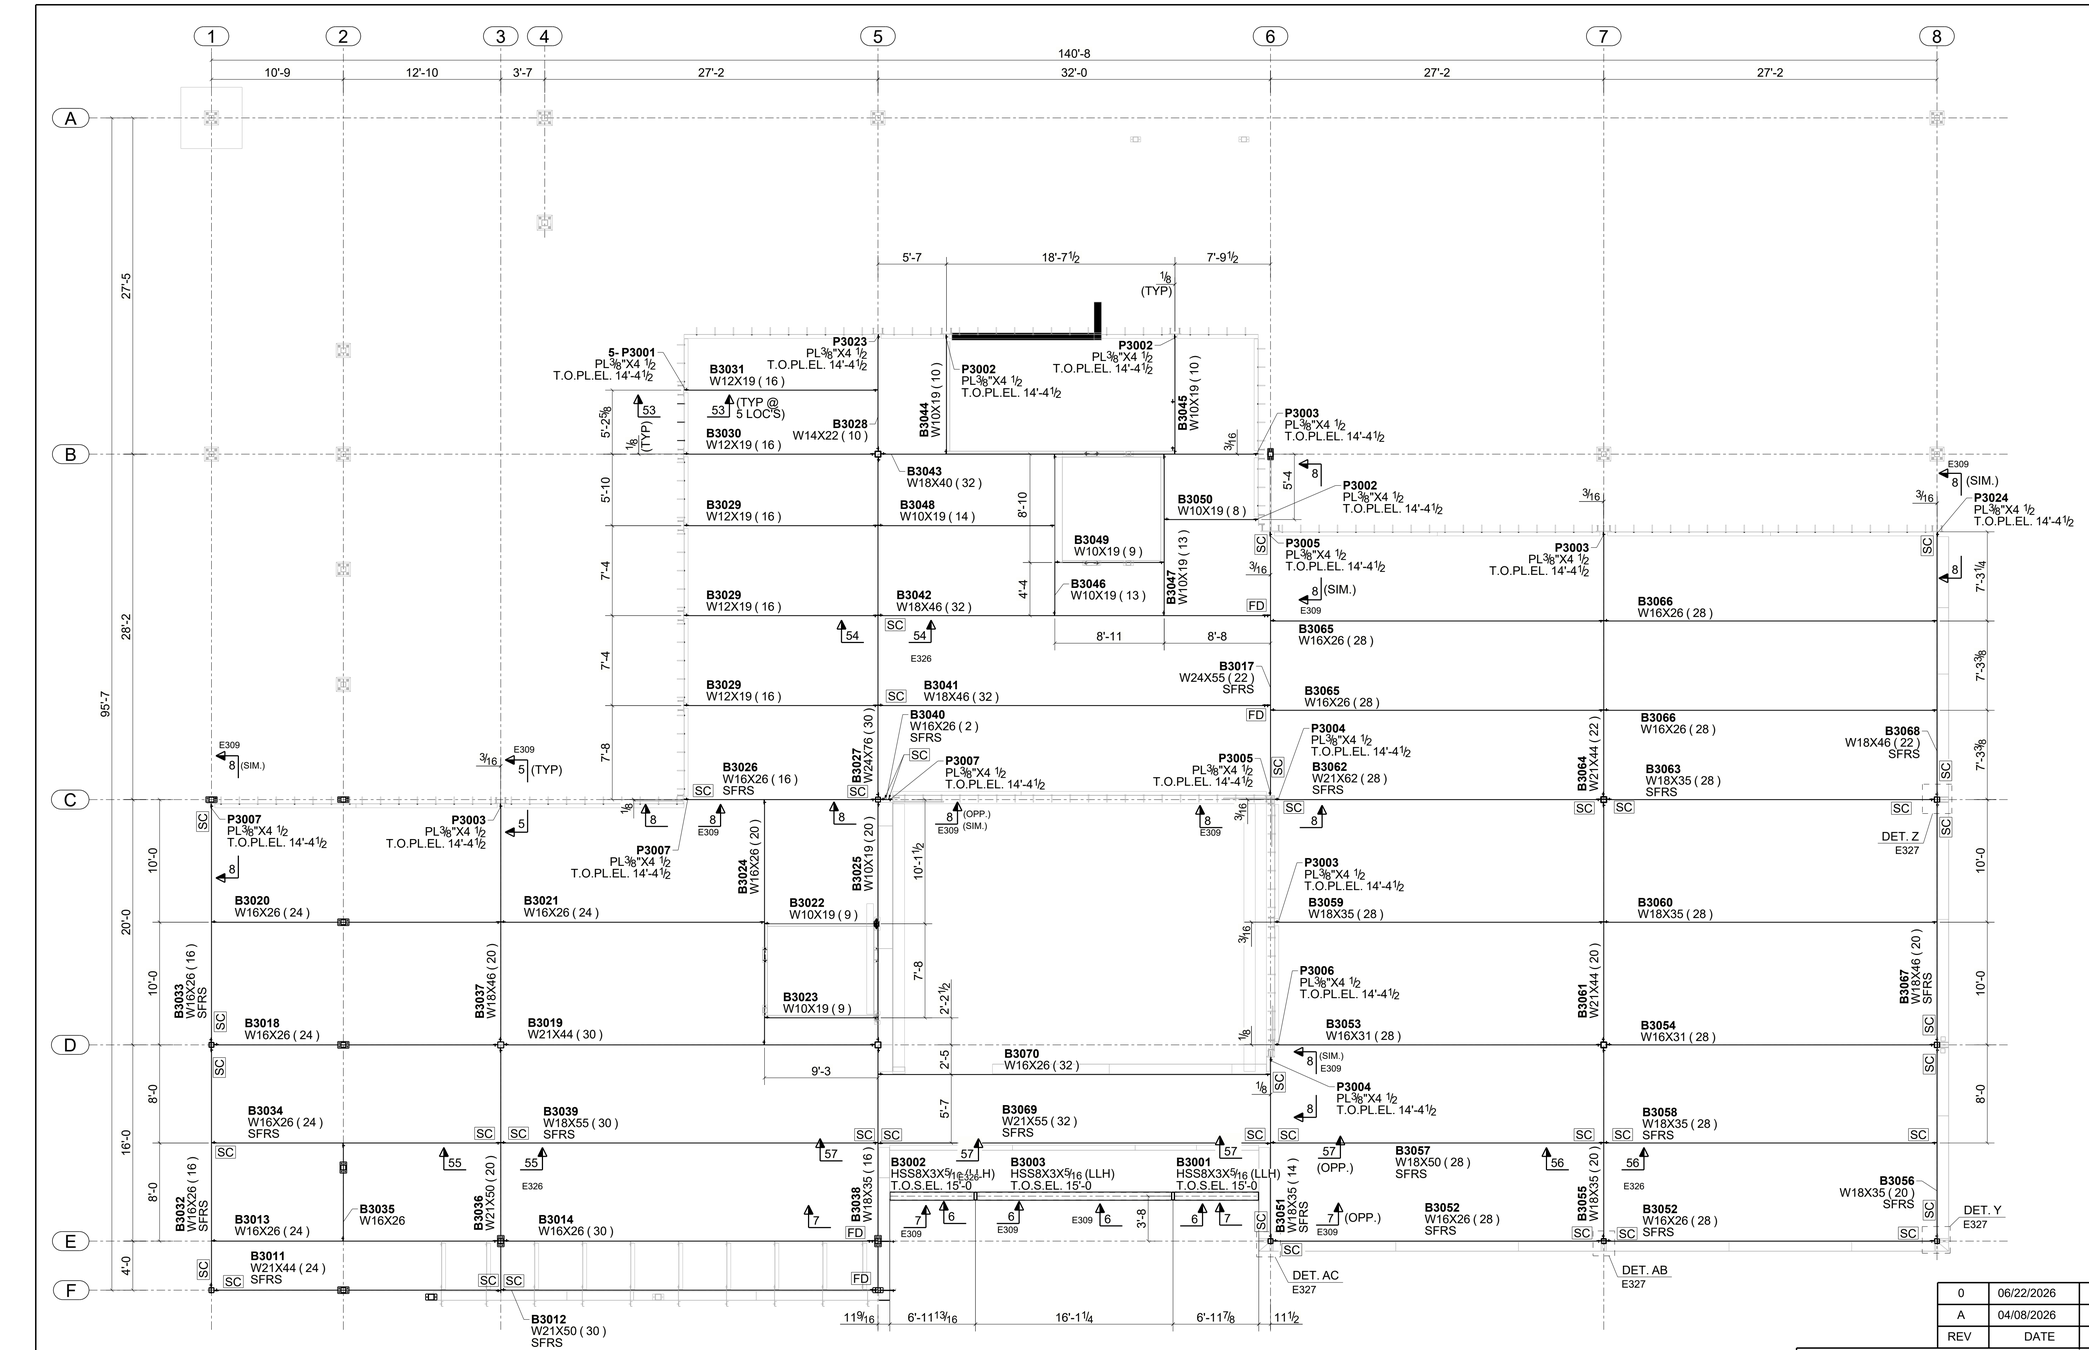

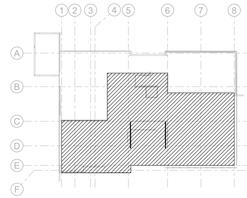

KEY PLAN

LEGEND:-

T.O.S.	-	TOP OF STEEL
EL.	-	ELEVATION
T.O.PL.	-	TOP OF PLATE
SC	-	SLIP CRITICAL

Release 7

REV	DATE	BY	DESCRIPTION
0	06/22/2026	CAP	FOR FIELD USE
A	04/08/2026	CAP	FOR APPROVAL

LEVEL 2 FLOOR FRAMING PLAN

(REF.: S1.2)

T.O.S. EL. 14'-6" (U.N.O.)


SPOKANE METALS STEEL FABRICATORS

18515 Garland Ave
Spokane Valley, WA 99027

DWG NAME: LEVEL 2 FLOOR FRAMING PLAN
FOR Morrow Court House
LOCATION 640 NE COURTHOUSE WAY
CONTRACTOR Bouton Construction Company
DRAWN 02/13/2026 BY YRM CHECKED 06/22/2026 BY ASC


CONT. NO.	DWG. NO.
26-09	E303

Tekla Structures

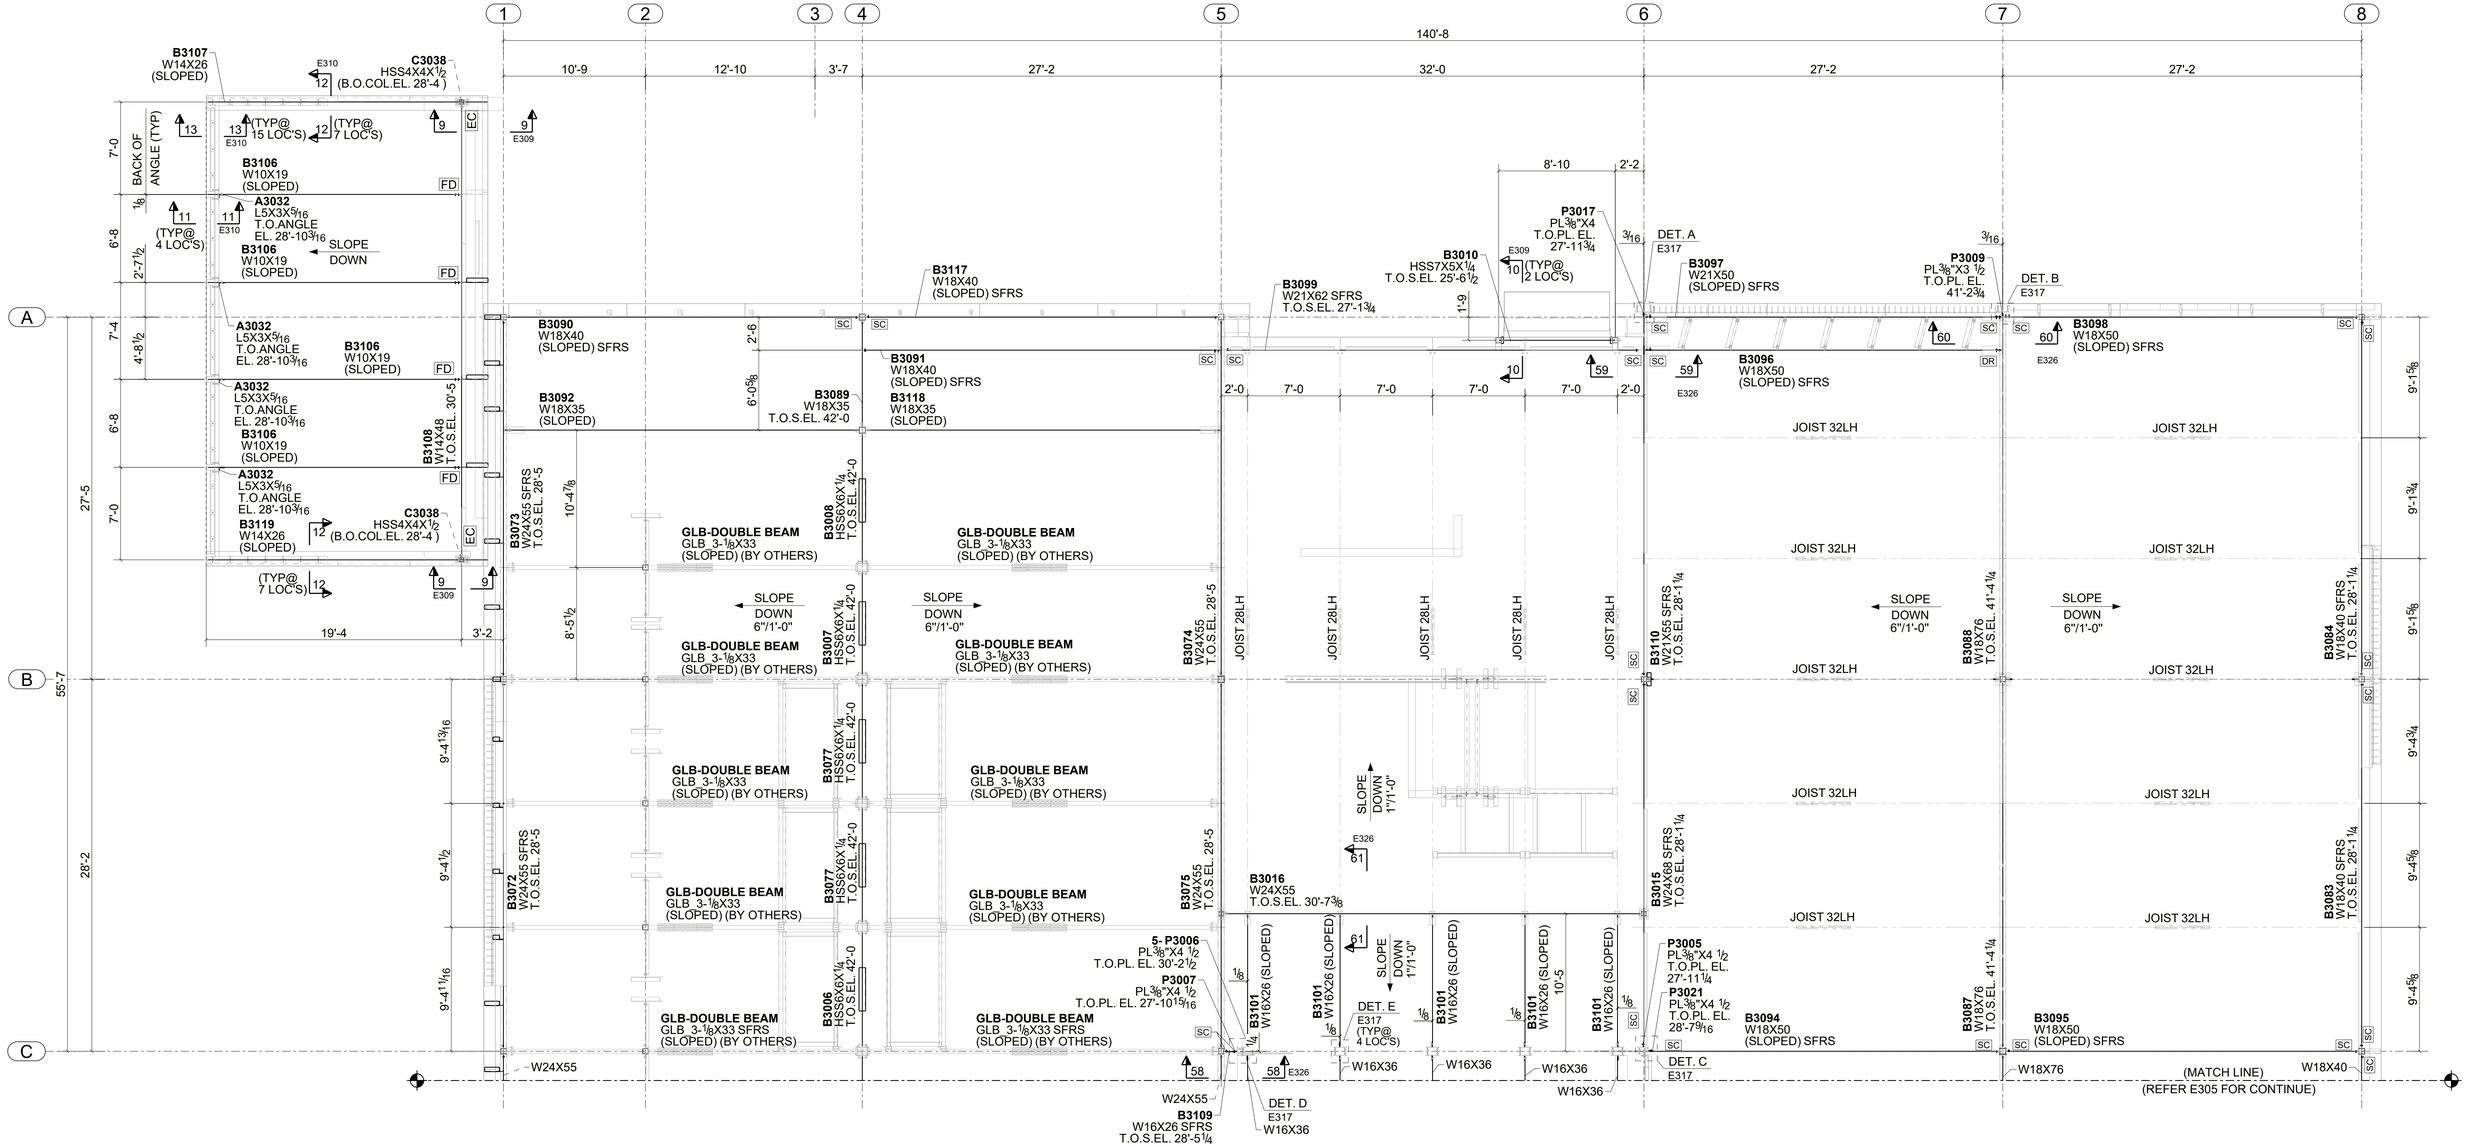

ROOF FRAMING PLAN

(REF.: S1.3)

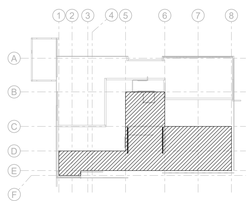

KEY PLAN

LEGEND:-

T.O.S. - TOP OF STEEL
EL. - ELEVATION

Release 7

REV	DATE	BY	DESCRIPTION
0	06/22/2026	CAP	FOR FIELD USE
A	04/08/2026	CAP	FOR APPROVAL


SPOKANE METALS
STEEL FABRICATORS

18515 Garland Ave
Spokane Valley, WA 99027


DWG NAME: ROOF FRAMING PLAN
FOR Morrow Court House
LOCATION 640 NE COURTHOUSE WAY
CONTRACTOR Bouton Construction Company
DRAWN 02/17/2026 BY YRM CHECKED 06/22/2026 BY ASC

CONT. NO.	DWG. NO.
26-09	E304

Tekla Structures

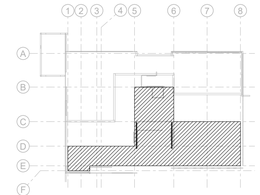

KEY PLAN

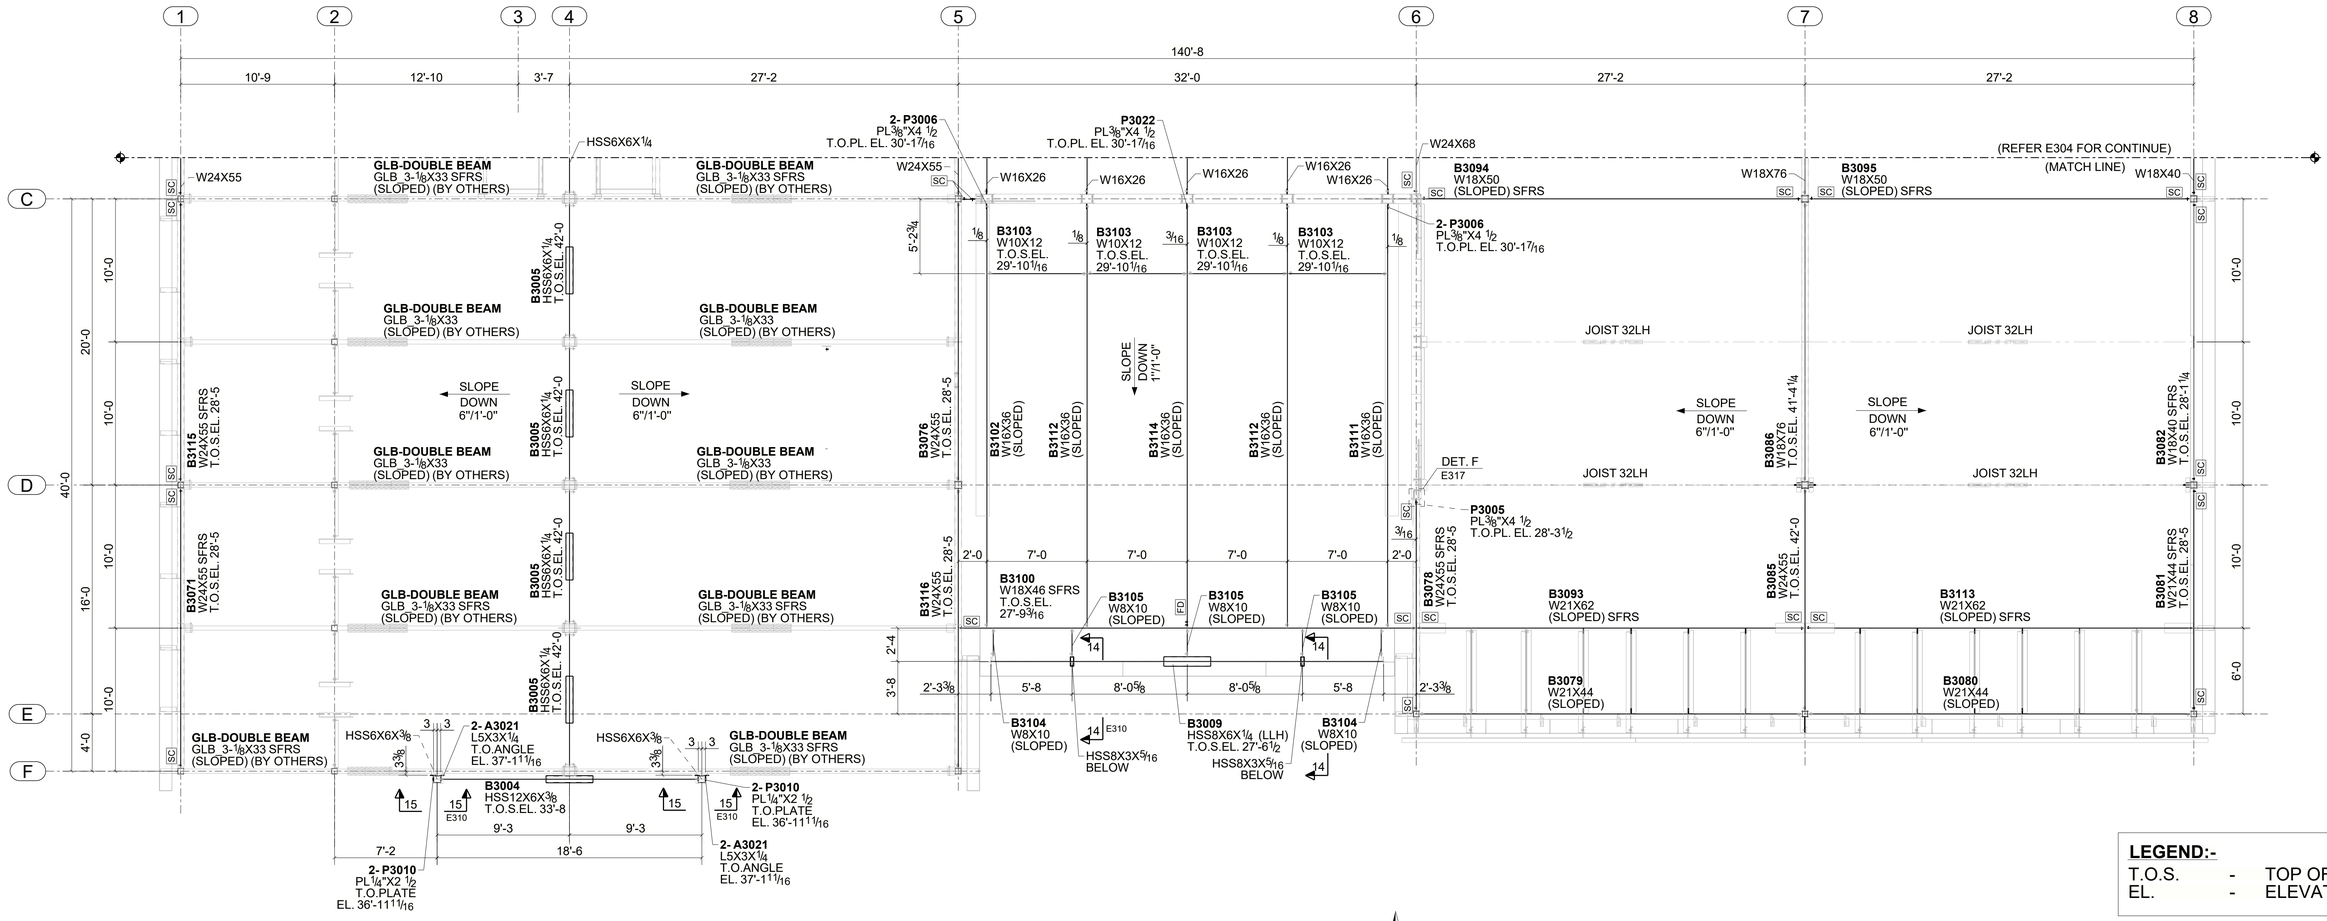

ROOF FRAMING PLAN

(REF.: S1.2)

LEGEND:-

T.O.S.	-	TOP OF STEEL
EL.	-	ELEVATION

Release 7

REV	DATE	BY	DESCRIPTION
0	06/22/2026	CAP	FOR FIELD USE
A	04/08/2026	CAP	FOR APPROVAL

SPOKANE METALS
STEEL FABRICATORS

18515 Garland Ave
Spokane Valley, WA 99027

DWG NAME: ROOF FRAMING PLAN
FOR Morrow Court House
LOCATION 640 NE COURTHOUSE WAY
CONTRACTOR Bouton Construction Company
DRAWN 02/17/2026 BY YRM CHECKED 06/22/2026 BY ASC

CONT. NO.	DWG. NO.
26-09	E305

Tekla Structures

LEVEL 2 FLOOR SLAB EDGE PLAN

(REF.: S1.2)

T.O.S. EL. 14'-6" (U.N.O.)

Release 7

REV	DATE	BY	DESCRIPTION
0	06/22/2026	CAP	FOR FIELD USE
A	04/08/2026	CAP	FOR APPROVAL

LEGEND:-

T.O.S.	-	TOP OF STEEL
EL.	-	ELEVATION
T.O.A.	-	TOP OF ANGLE

KEY PLAN

SPOKANE METALS STEEL FABRICATORS

18515 Garland Ave
Spokane Valley, WA 99027

DWG NAME: LEVEL 2 SLAB EDGE PLAN
FOR Morrow Court House
LOCATION 640 NE COURTHOUSE WAY
CONTRACTOR Bouton Construction Company
DRAWN 02/17/2026 BY YRM CHECKED 06/22/2026 BY ASC


CONT. NO. 26-09

DWG. NO. E306

Tekla Structures

ROOF SLAB EDGE PLAN

(REF.: S1.3)
T.O.S. EL. 42'-0" (U.N.O.)

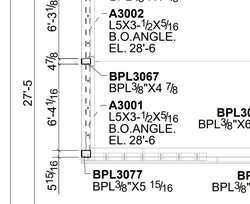

KEY PLAN

LEGEND:-

T.O.S.	-	TOP OF STEEL
EL.	-	ELEVATION

Release 7

REV	DATE	BY	DESCRIPTION
0	06/22/2026	CAP	FOR FIELD USE
A	04/08/2026	CAP	FOR APPROVAL


SPOKANE METALS
STEEL FABRICATORS


18515 Garland Ave
Spokane Valley, WA 99027

DWG NAME: ROOF SLAB EDGE PLAN
FOR Morrow Court House
LOCATION 640 NE COURTHOUSE WAY
CONTRACTOR Bouton Construction Company
DRAWN 02/17/2026 BY YRM CHECKED 06/22/2026 BY ASC

CONT. NO.	DWG. NO.
26-09	E307

Tekla Structures

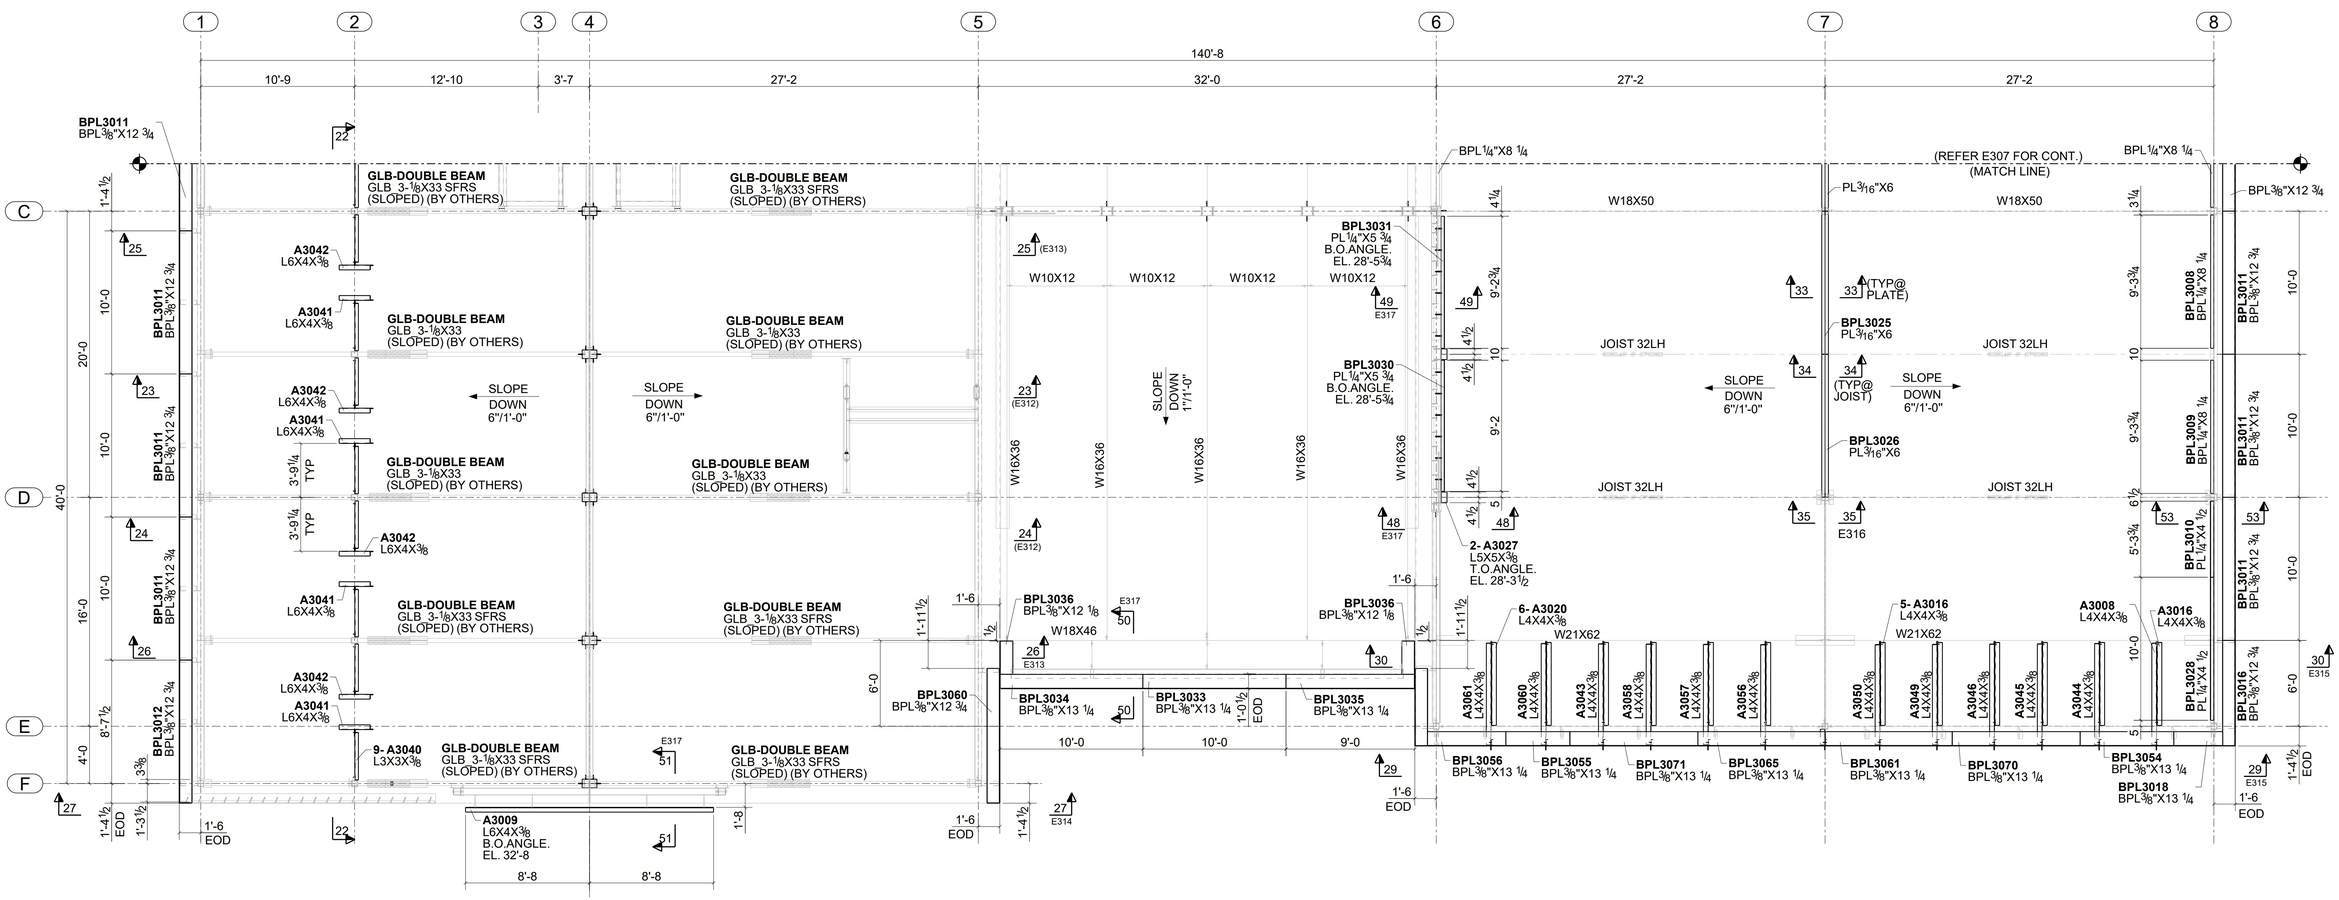

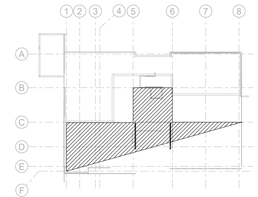

KEY PLAN

ROOF SLAB EDGE PLAN

(REF.: S1.3)

T.O.S. EL. 42'-0" (U.N.O.)

LEGEND:-

T.O.S.	-	TOP OF STEEL
EL.	-	ELEVATION

Release 7

REV	DATE	BY	DESCRIPTION
0	06/22/2026	CAP	FOR FIELD USE
A	04/08/2026	CAP	FOR APPROVAL

SPOKANE METALS
STEEL FABRICATORS

18515 Garland Ave
Spokane Valley, WA 99027

DWG NAME: ROOF SLAB EDGE PLAN
FOR Morrow Court House
LOCATION 640 NE COURTHOUSE WAY
CONTRACTOR Bouton Construction Company
DRAWN 02/17/2026 BY YRM CHECKED 06/22/2026 BY ASC

CONT. NO.	DWG. NO.
26-09	E308

Tekla Structures